


Barreira Hidráulica - Pump & Treat

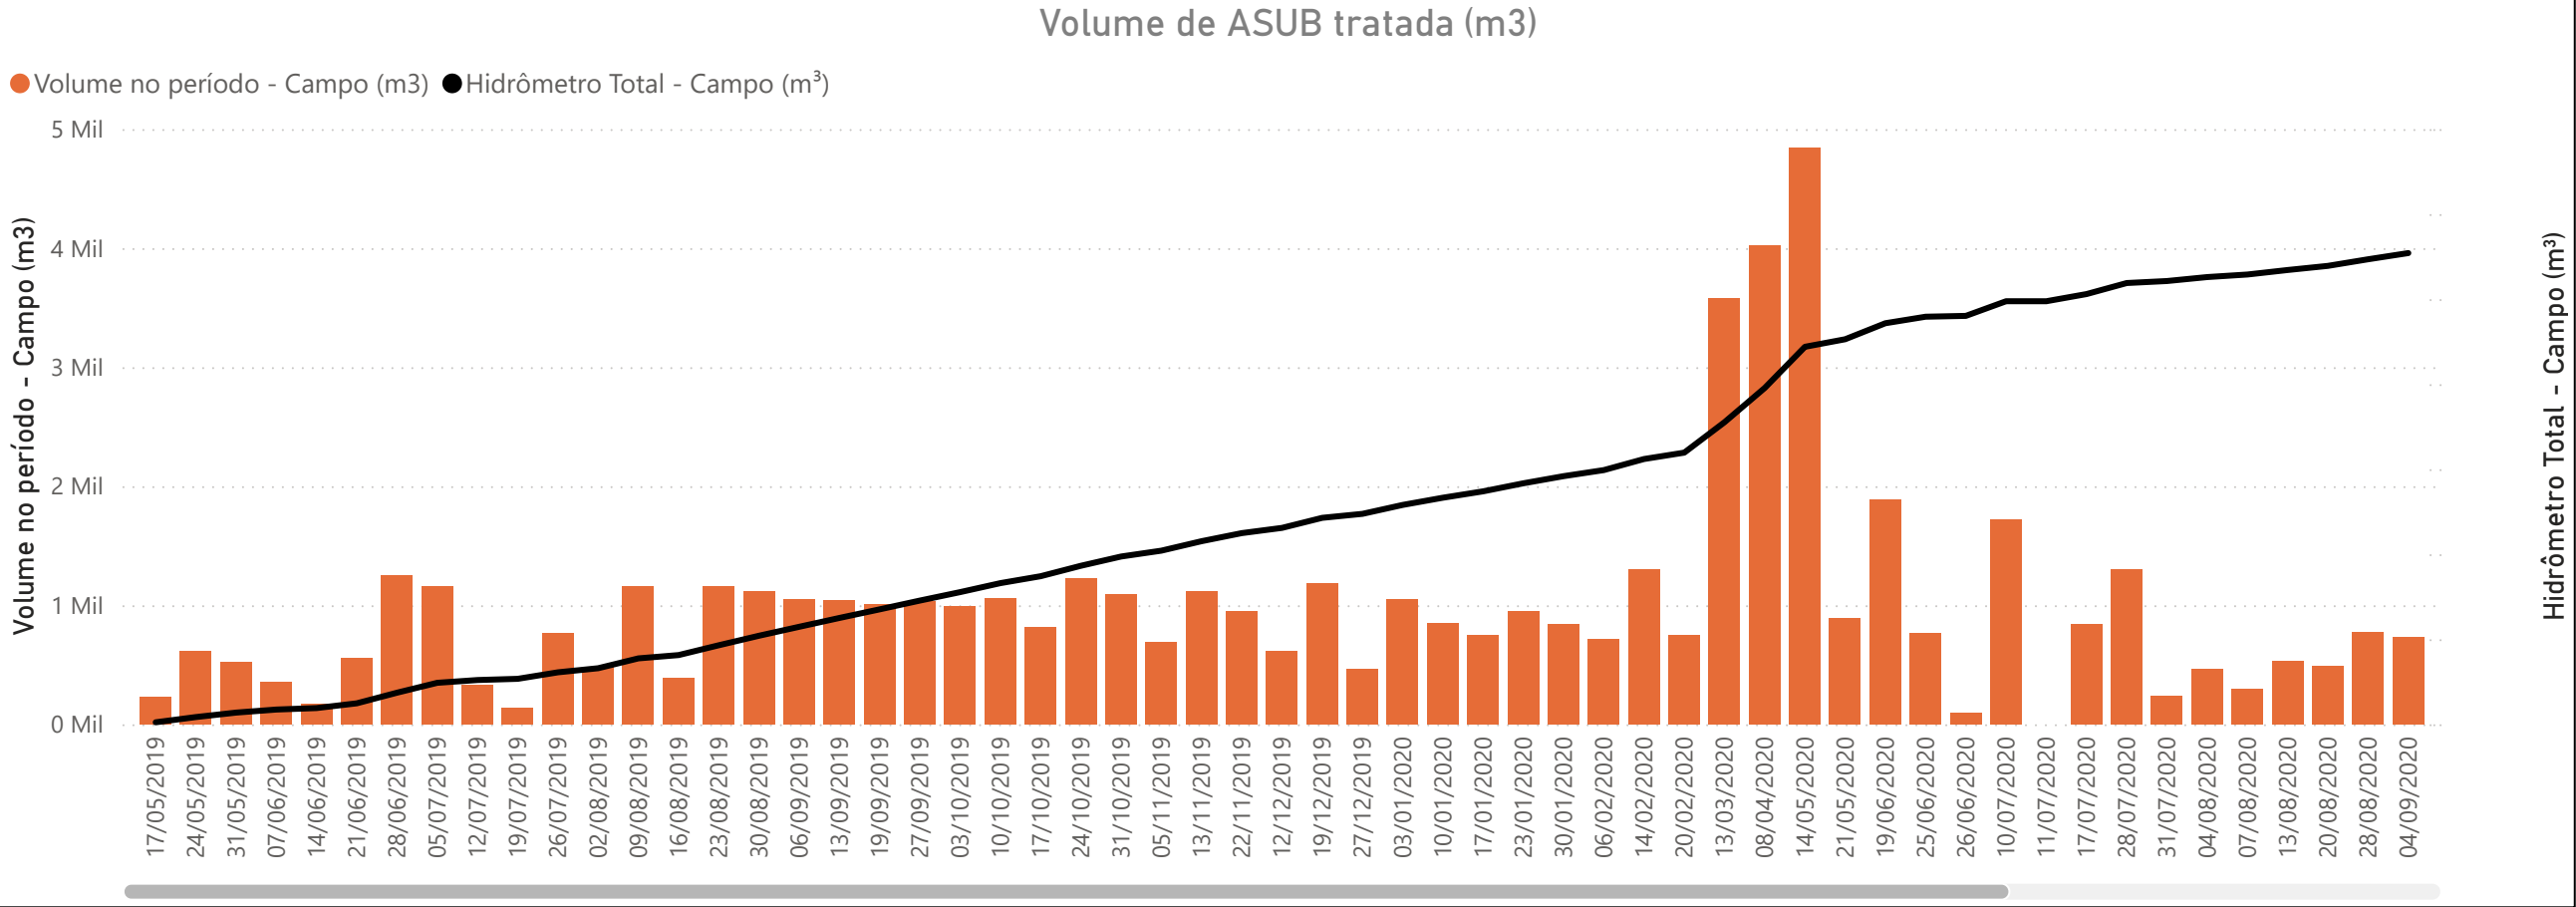

Data do Monitoramento



5/17/2019 12/30/2020



Volume Total Tratado (m³)

65.08 Mil

Vazão média Bombeamento (m³/h)

8.28

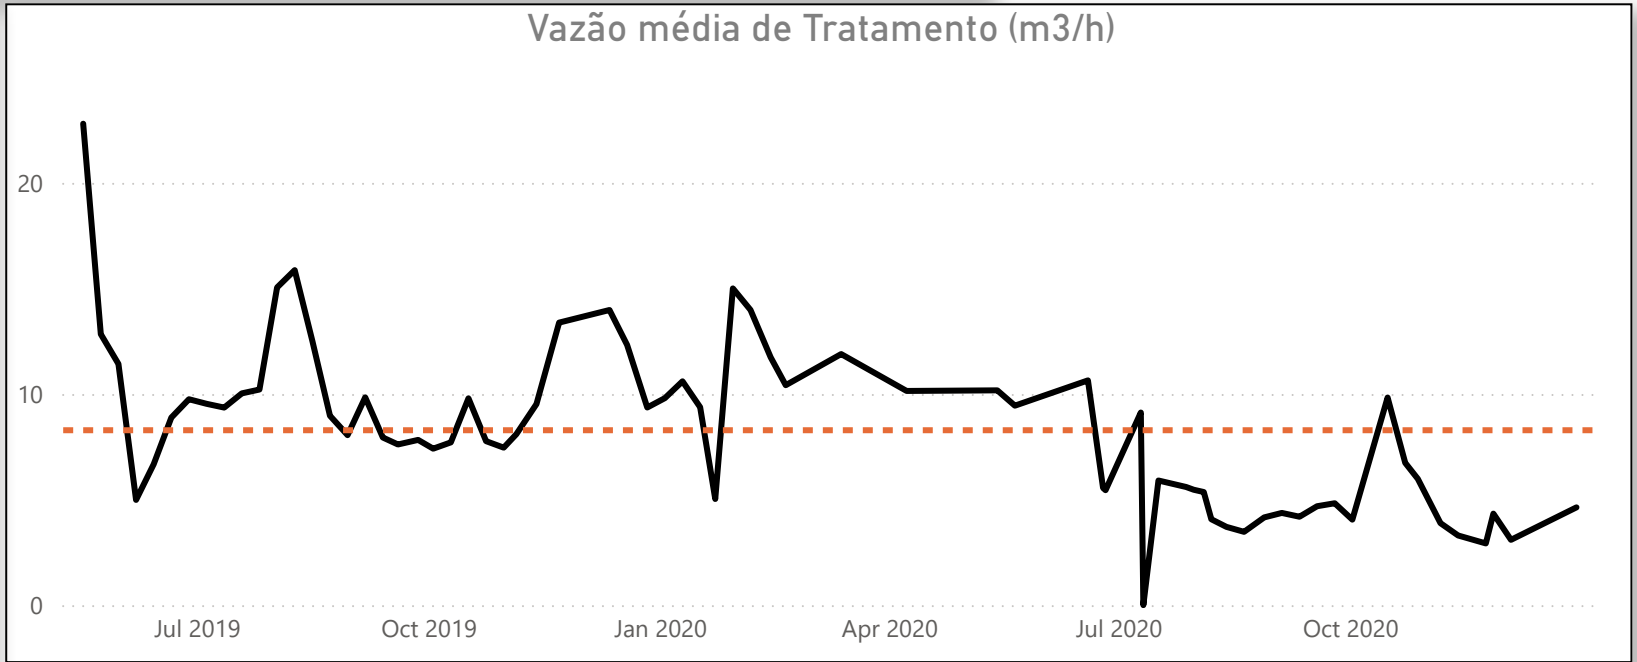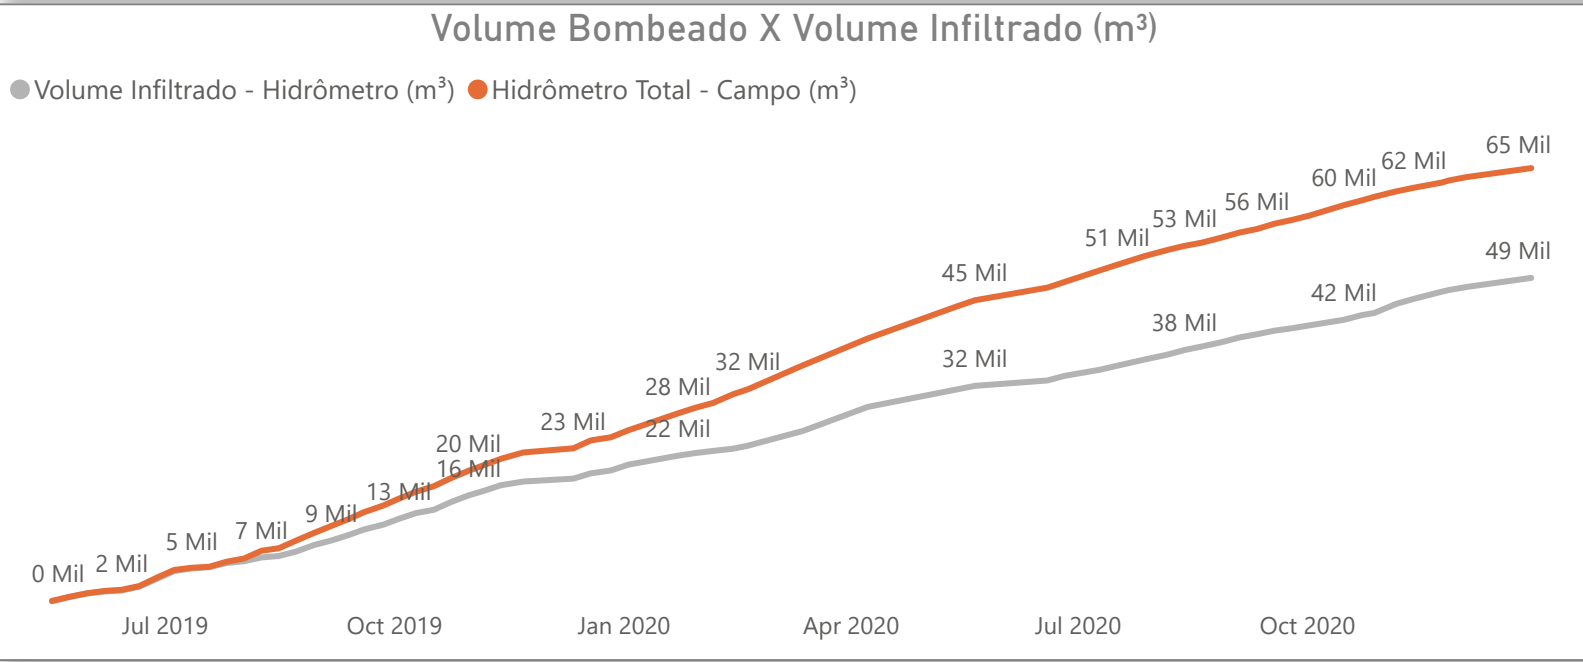

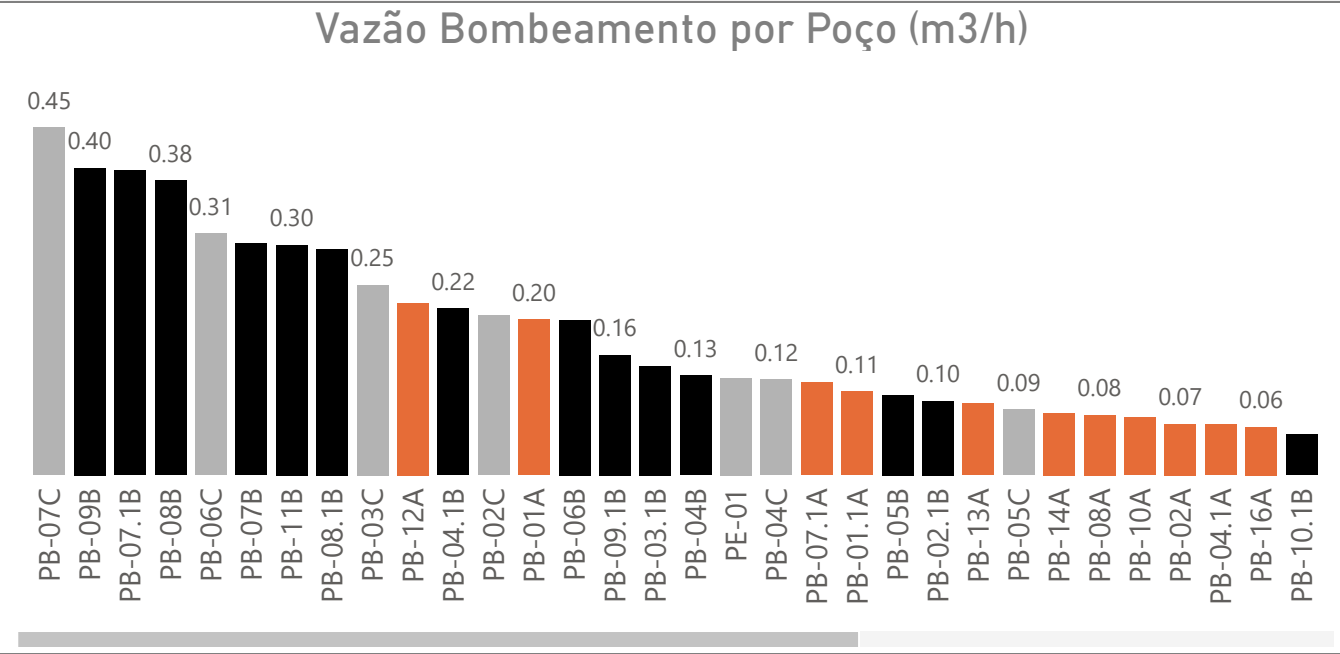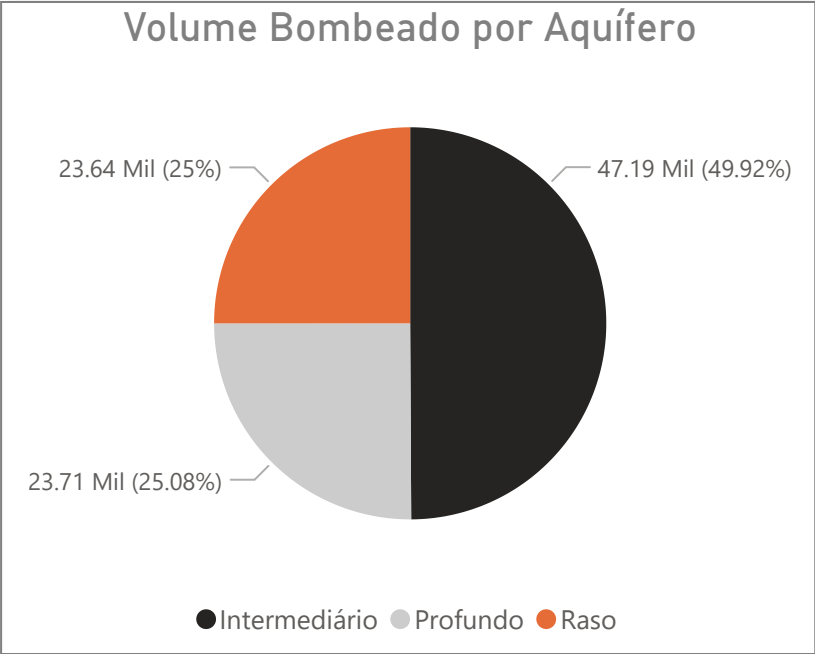

Soma Hidrômetros PBs (m3)


94.54 Mil

Vazão Média dos PBs (m3/h)

0.13

Maior Volume Bombeado

PB-07C

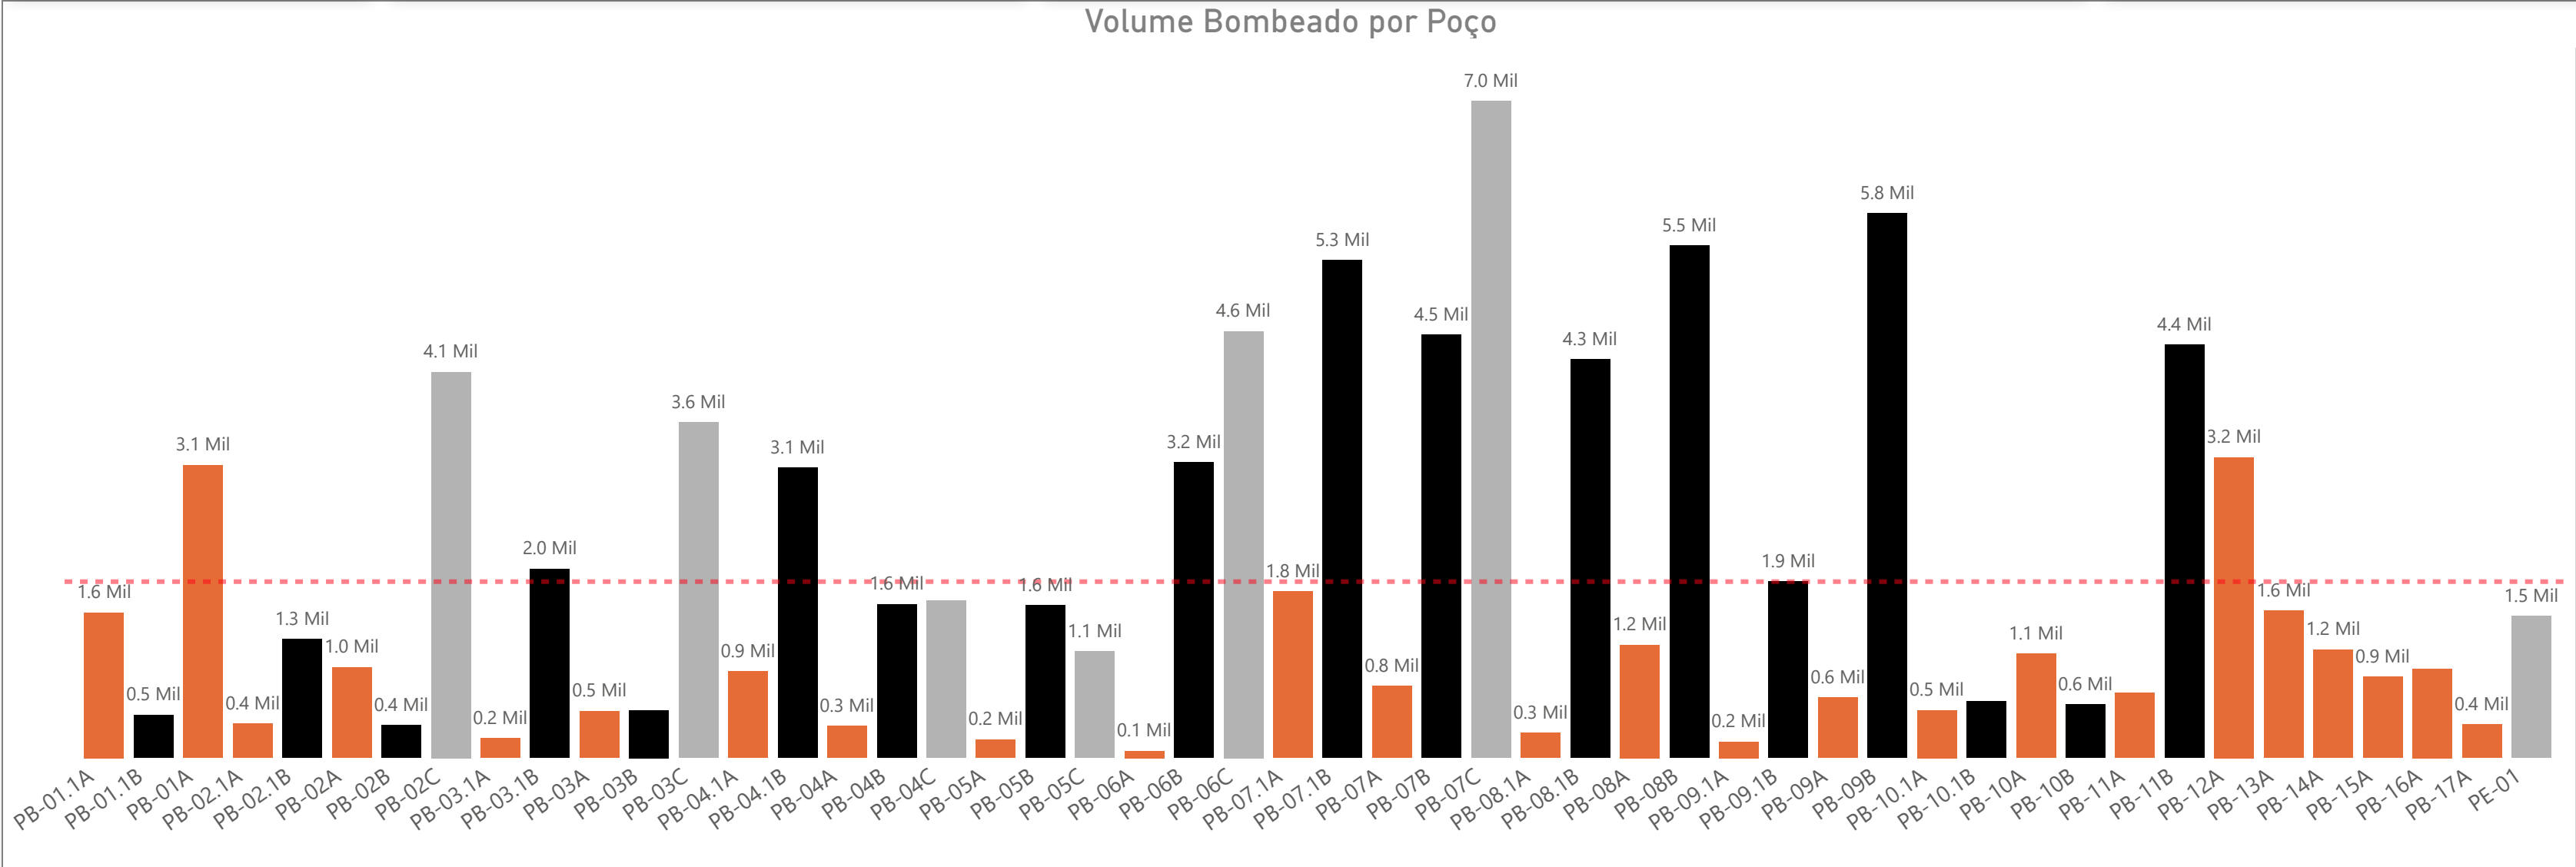

Data

5/17/2019

12/30/2020

Poço de Injeção

PI-01

PI-06

PI-02

PI-07


PI-03

PI-08

PI-04

PI-09

PI-05

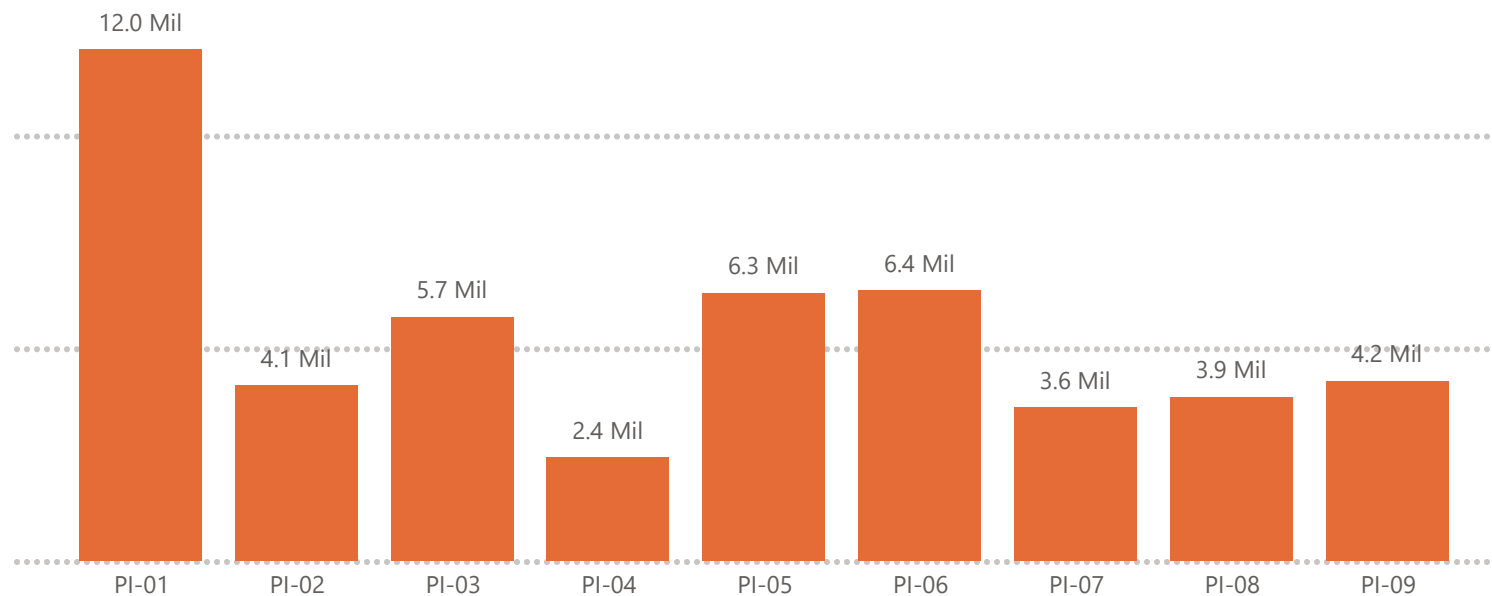Volume Total Infiltrado por Poço de Injeção (m³)Total Infiltrado (m³)


48.63 Mil




Total Descartado (m³)

24.12 Mil


% de Descarte do Total

33.15%

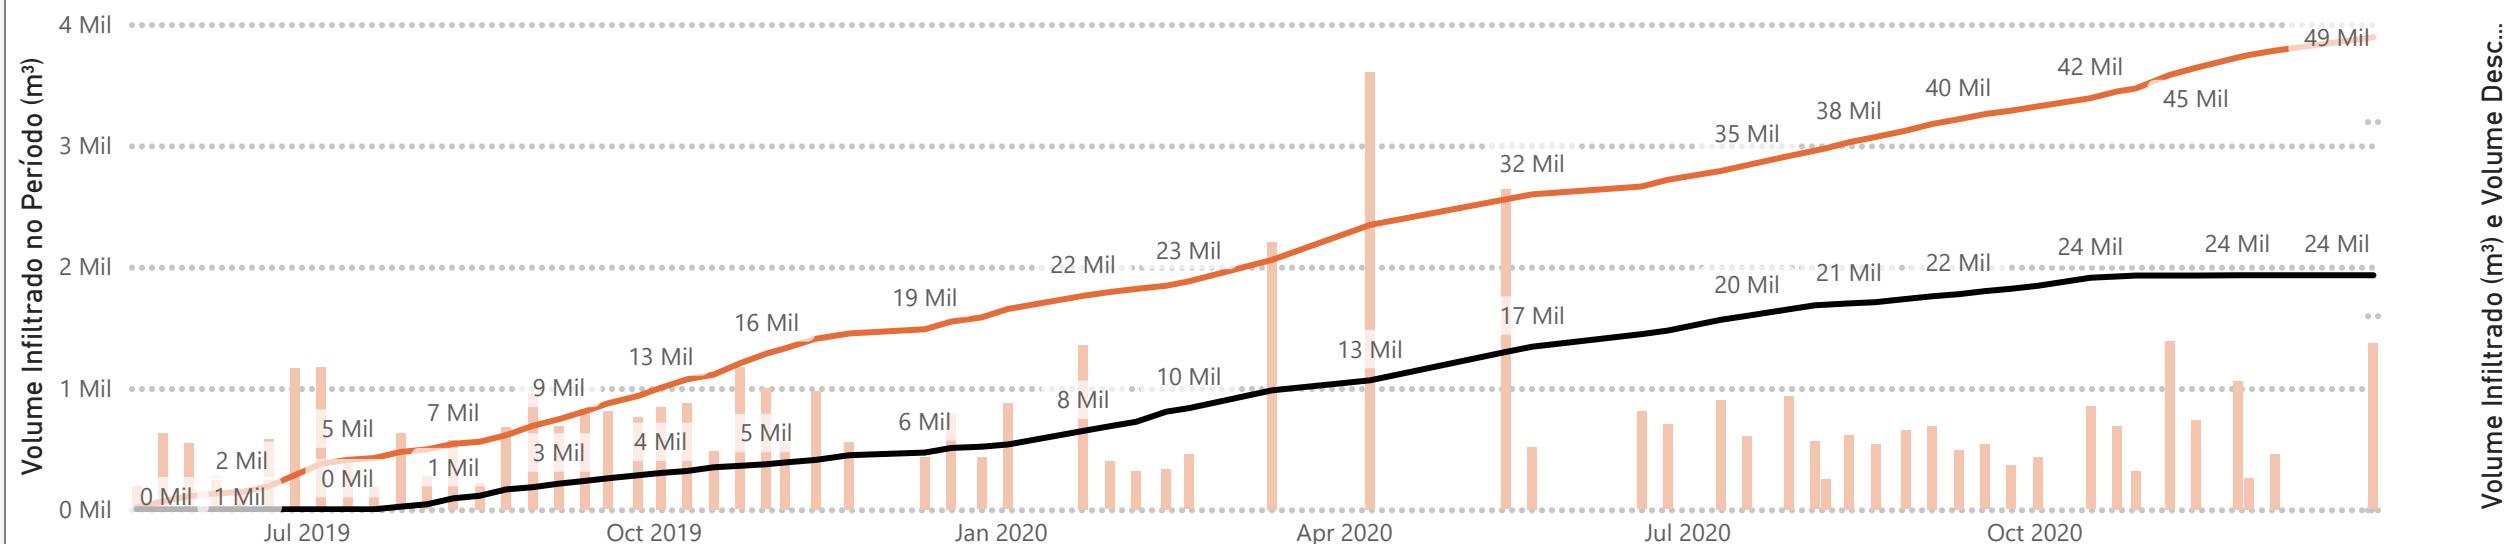
Volume Infiltrado e de Descarte (m³)● Volume Infiltrado no Período (m³) ● Volume Infiltrado (m³) ● Volume Descarte (m³)

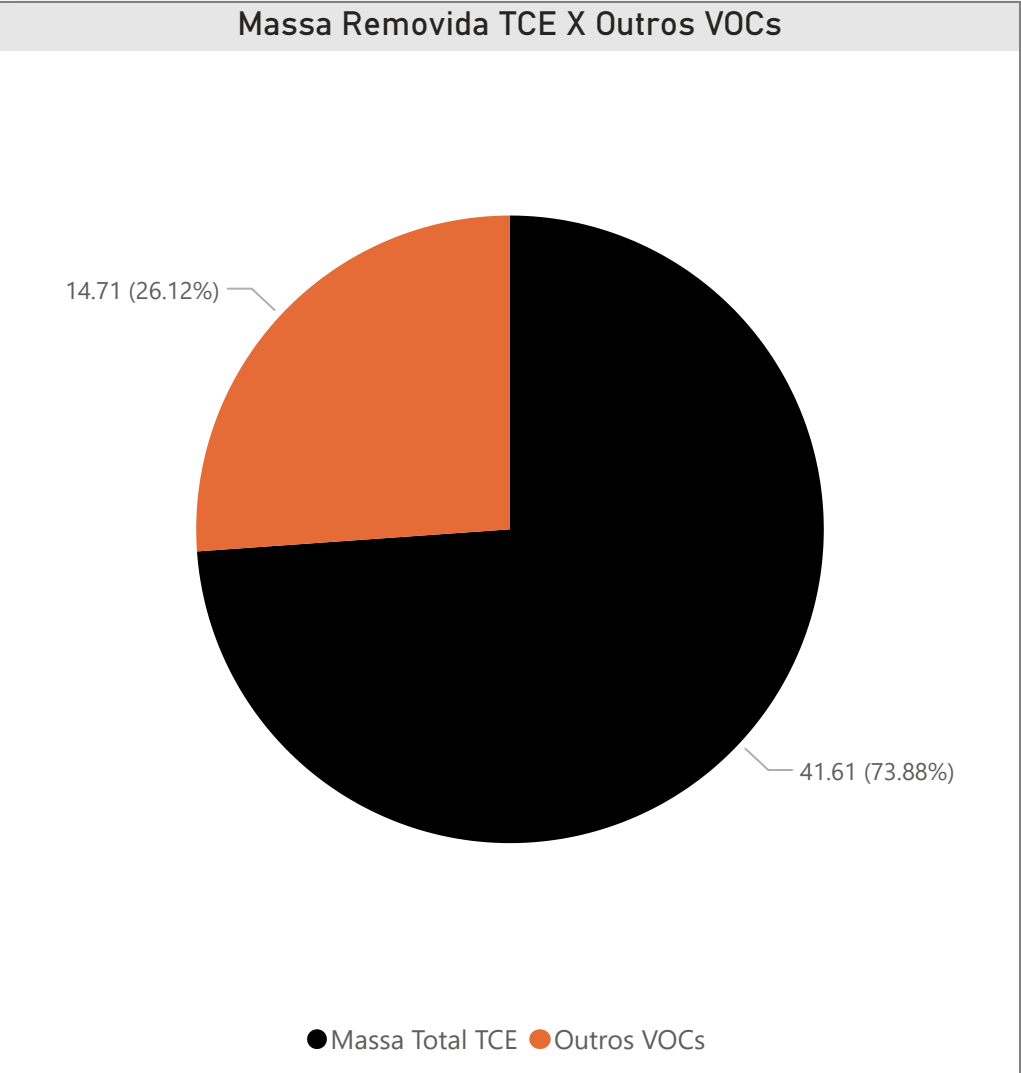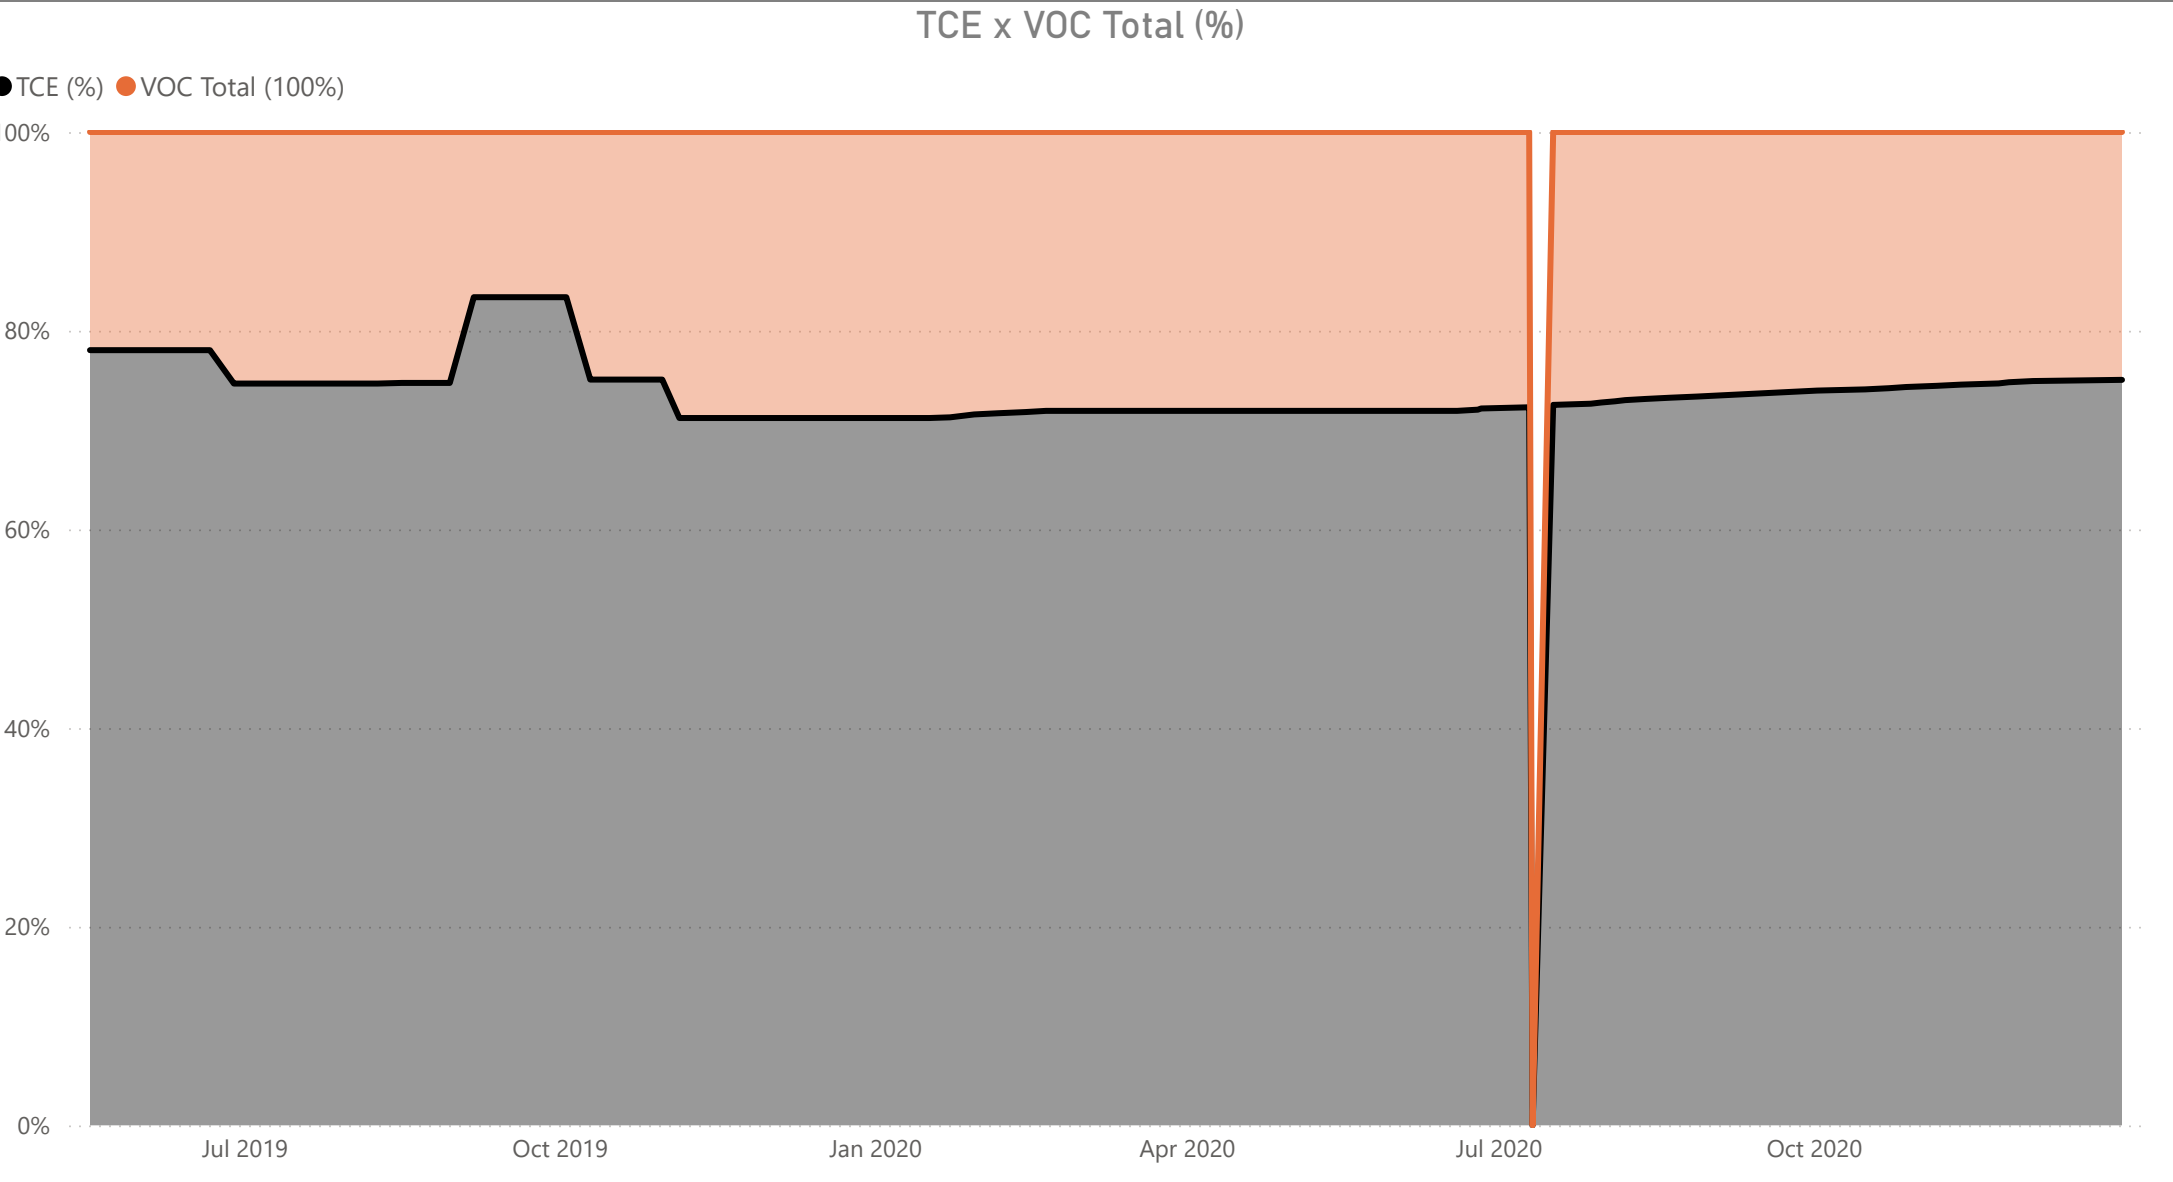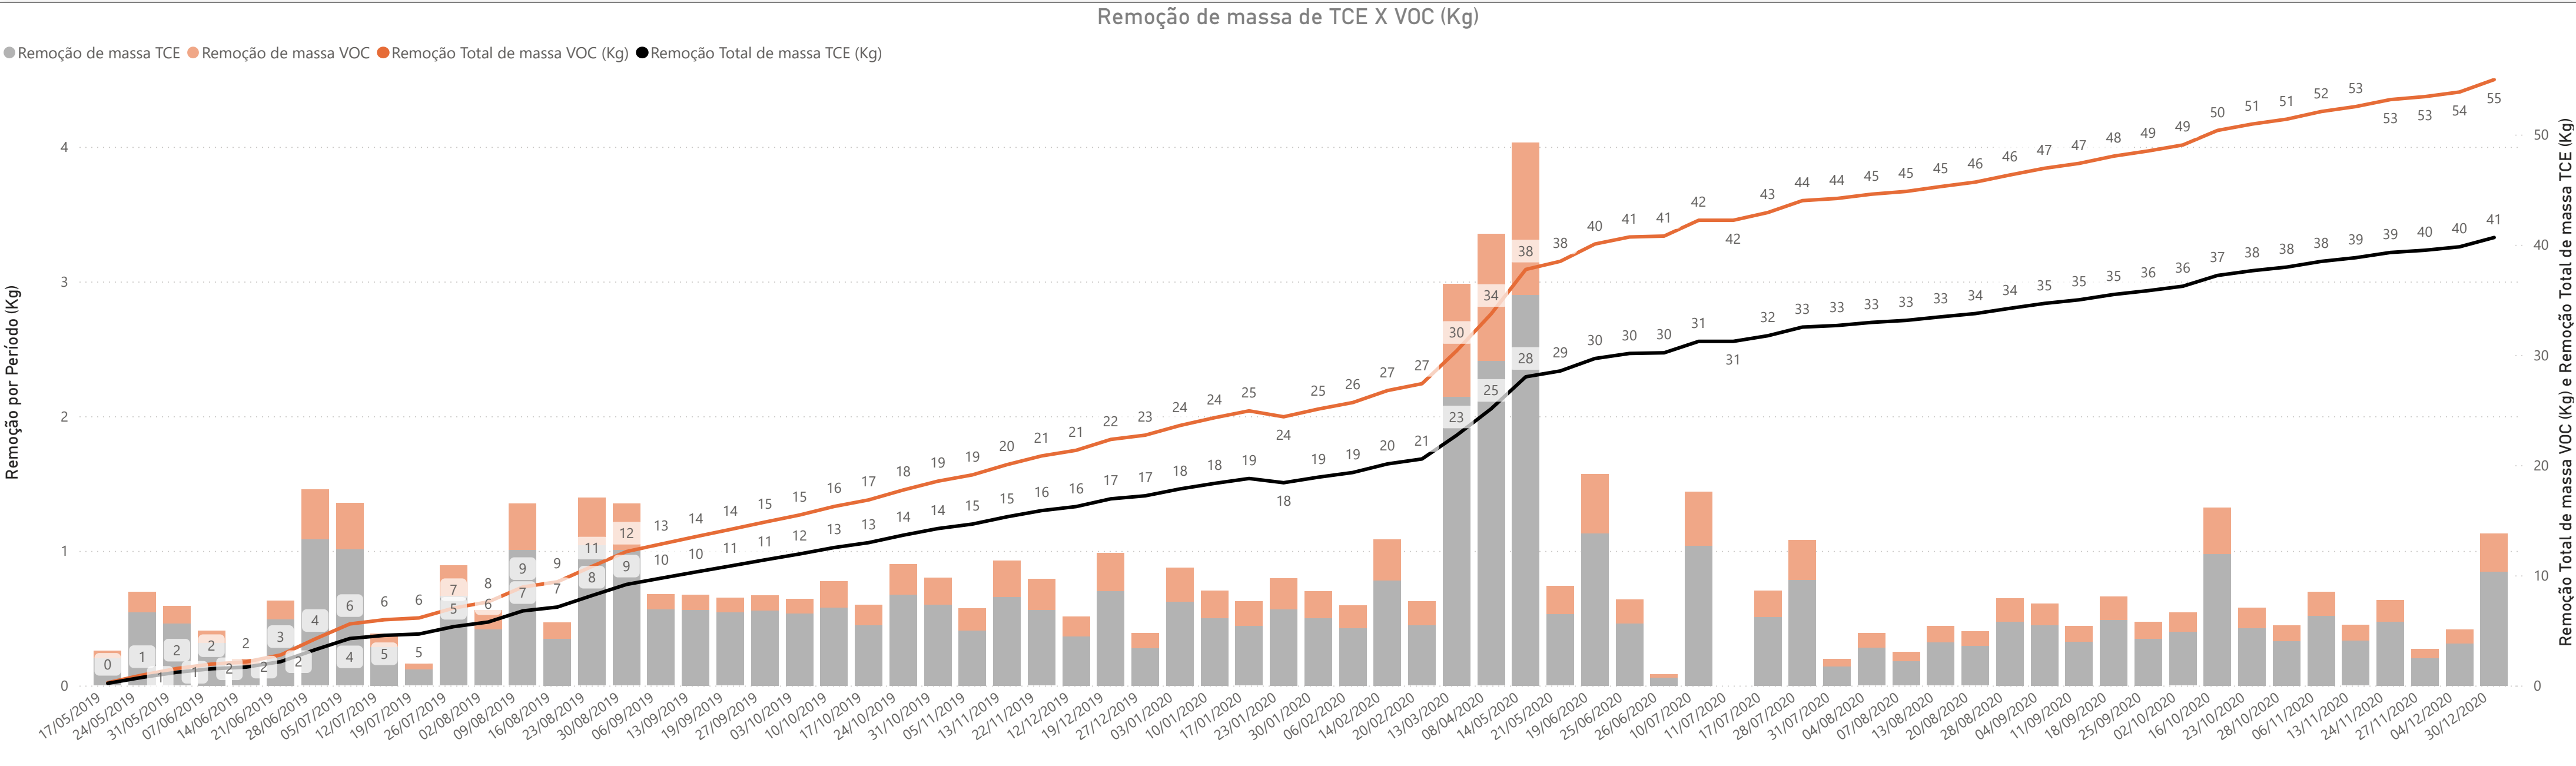


Pressão Linha Ar Comprimido (bar)

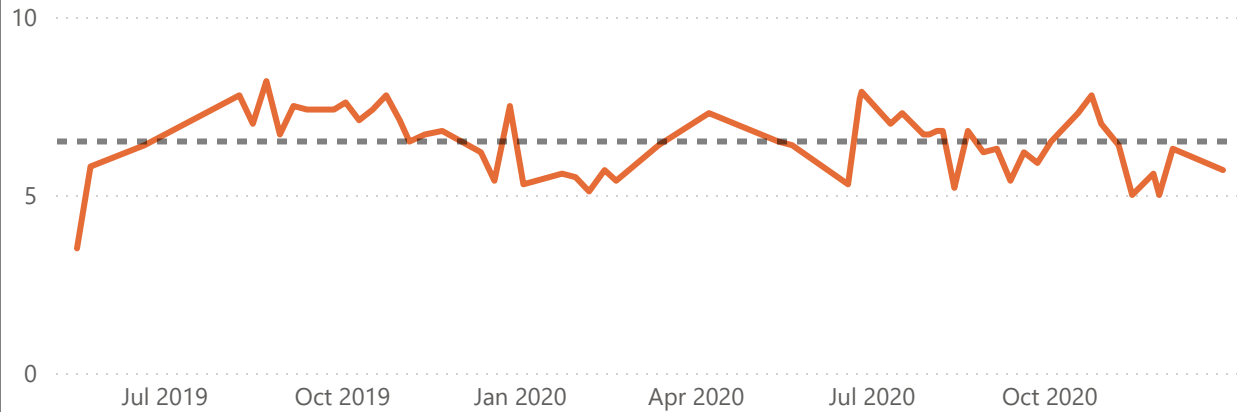

Pressão Bomba Infiltração - BH-102 (psi)

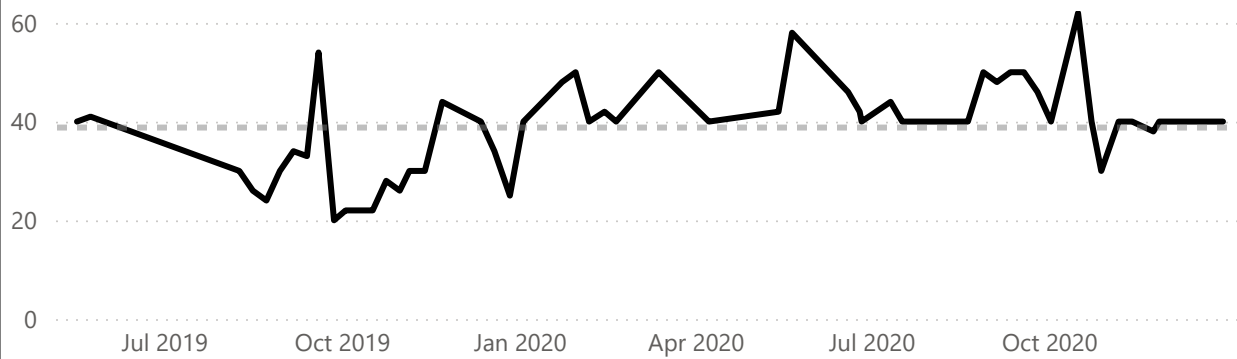

Pressão e Vazão Bomba de Carga (BT-2101)

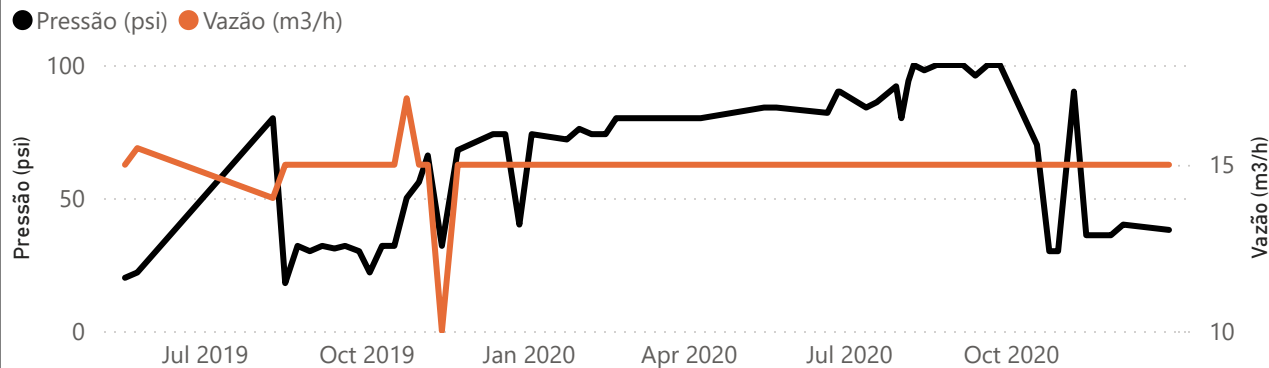

5/17/2019

12/30/2020

Horímetro Compressor

12.440 Mil

Média Pressão Reservatório CP (bar)

5.5


Média Vazão Infiltração (m3/h)

8.3

Média Drenagem do Compressor (l)

46.0

Pressão Filtro-bag (psi)

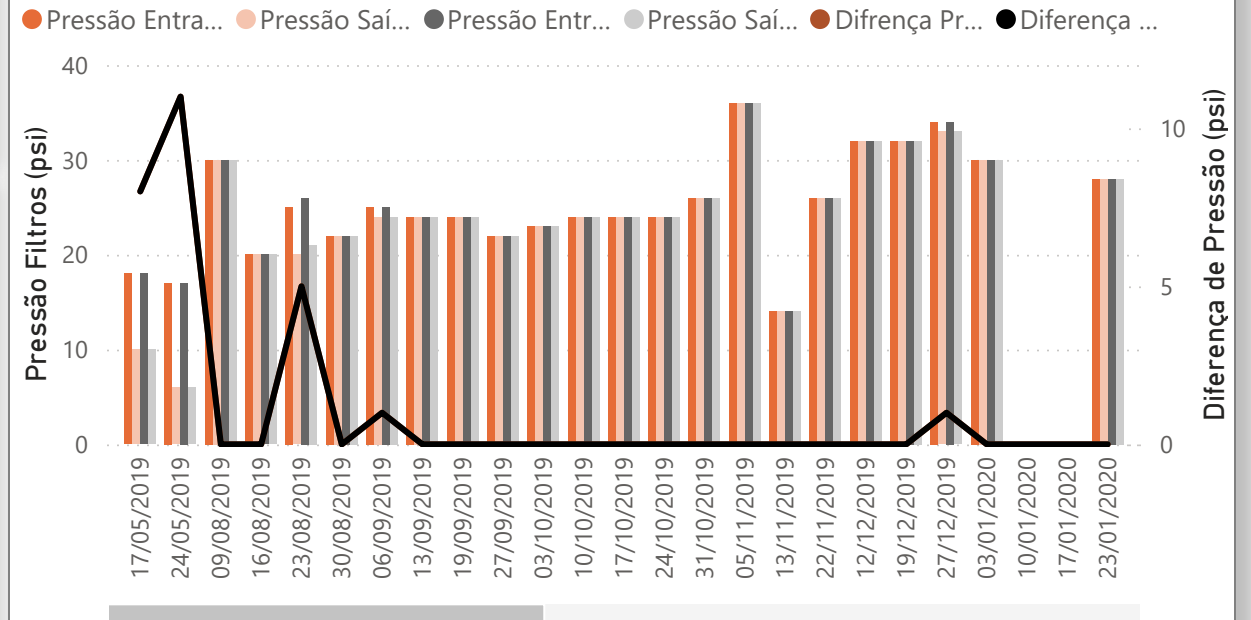


5/17/2019


12/30/2020

PID Colunas de Carvão (ppmv)

● PID Entrada FG-502 (ppmv) ● PID Entrada FG-501 (ppmv) ● PID Saída Sistema (ppmv)

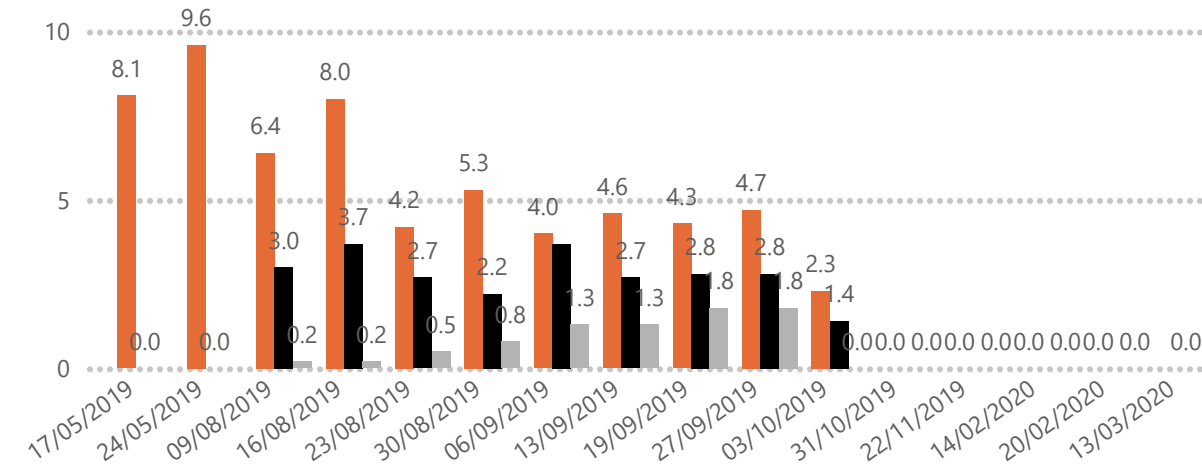


Eficiência Tratamento Colunas de Carvão Vapor

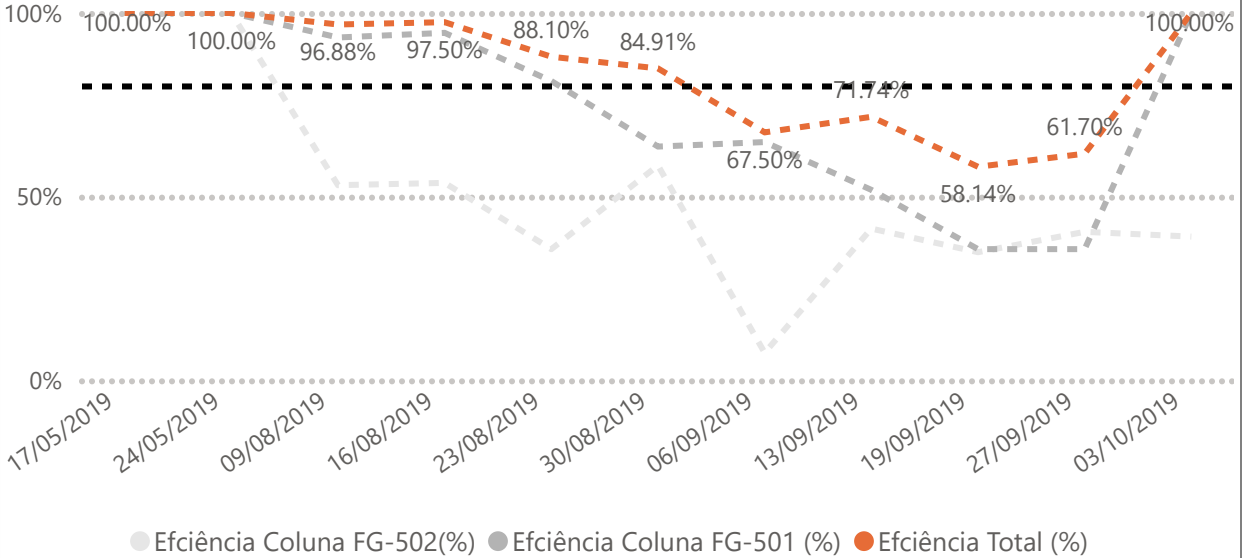


Diferença de Temperatura Colunas de Carvão Vapor (°C)

● Dif Temperatura FG-501 ● Dif Temperatura FG-502

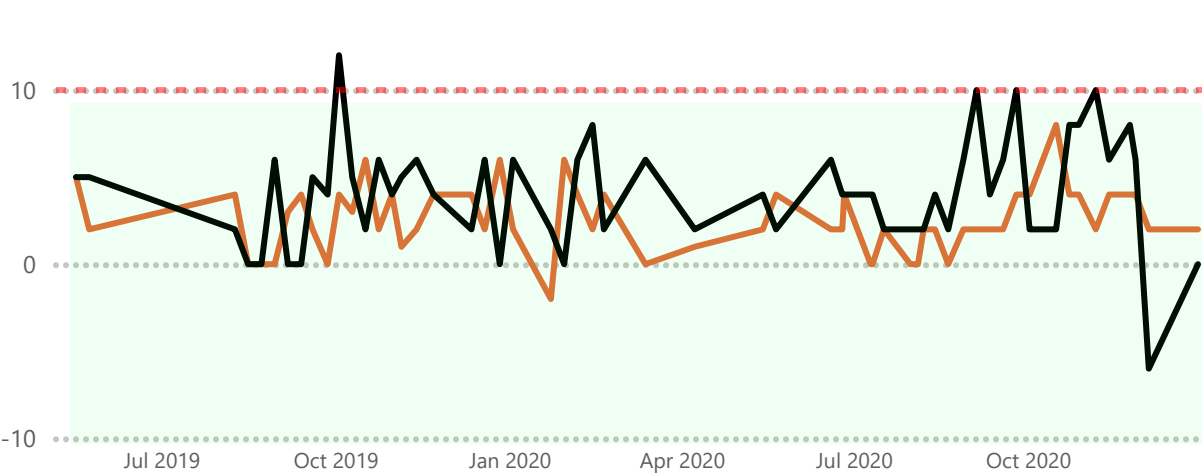

Pressão Colunas de Tratamento de Água (psi)

● Entrada FA-1301 ● Saída FA-1301 ● Entrada FA-1302 ● Saída FA-1302

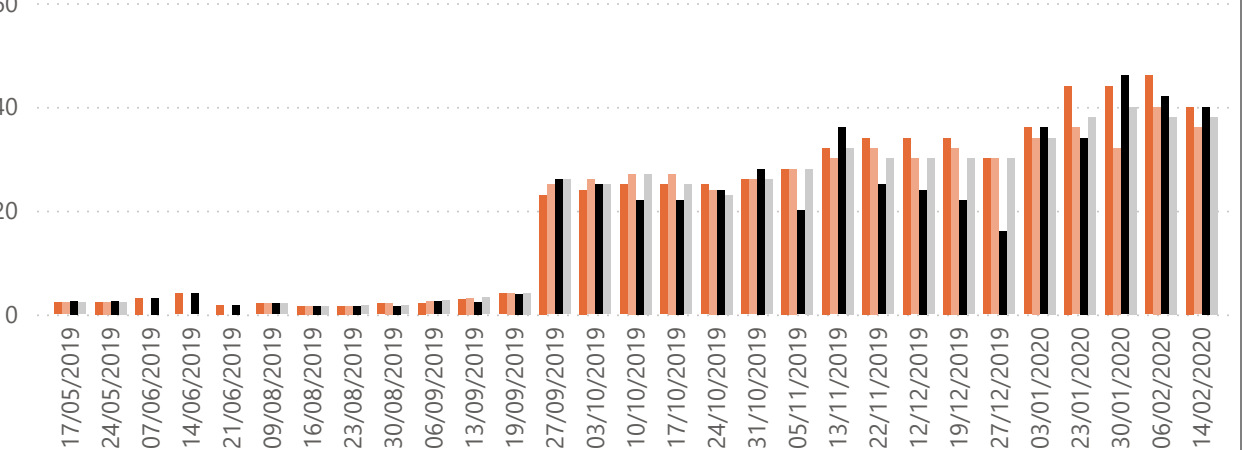

Aquífero

Intermediário

Profundo

Raso

Poço de Bom...


- ☐ PB-01.1A
- ☐ PB-01.1B
- ☐ PB-01A
- ☐ PB-02.1A
- ☐ PB-02.1B
- ☐ PB-02A
- ☐ PB-02B
- ☐ PB-02C
- ☐ PB-03.1A
- ☐ PB-03.1B
- ☐ PB-03A
- ☐ PB-03B
- ☐ PB-03C
- ☐ PB-04.1A
- ☐ PB-04.1B
- ☐ PB-04A
- ☐ PB-04B
- ☐ PB-04C
- ☐ PB-05A
- ☐ PB-05B
- ☐ PB-05C
- ☐ PB-06A
- ☐ PB-06B
- ☐ PB-06C
- ☐ PB-07.1A
- ☐ PB-07.1B

Data


5/17/2019

12/30/2020

Volume Bombeado por Período por Poço (m3)

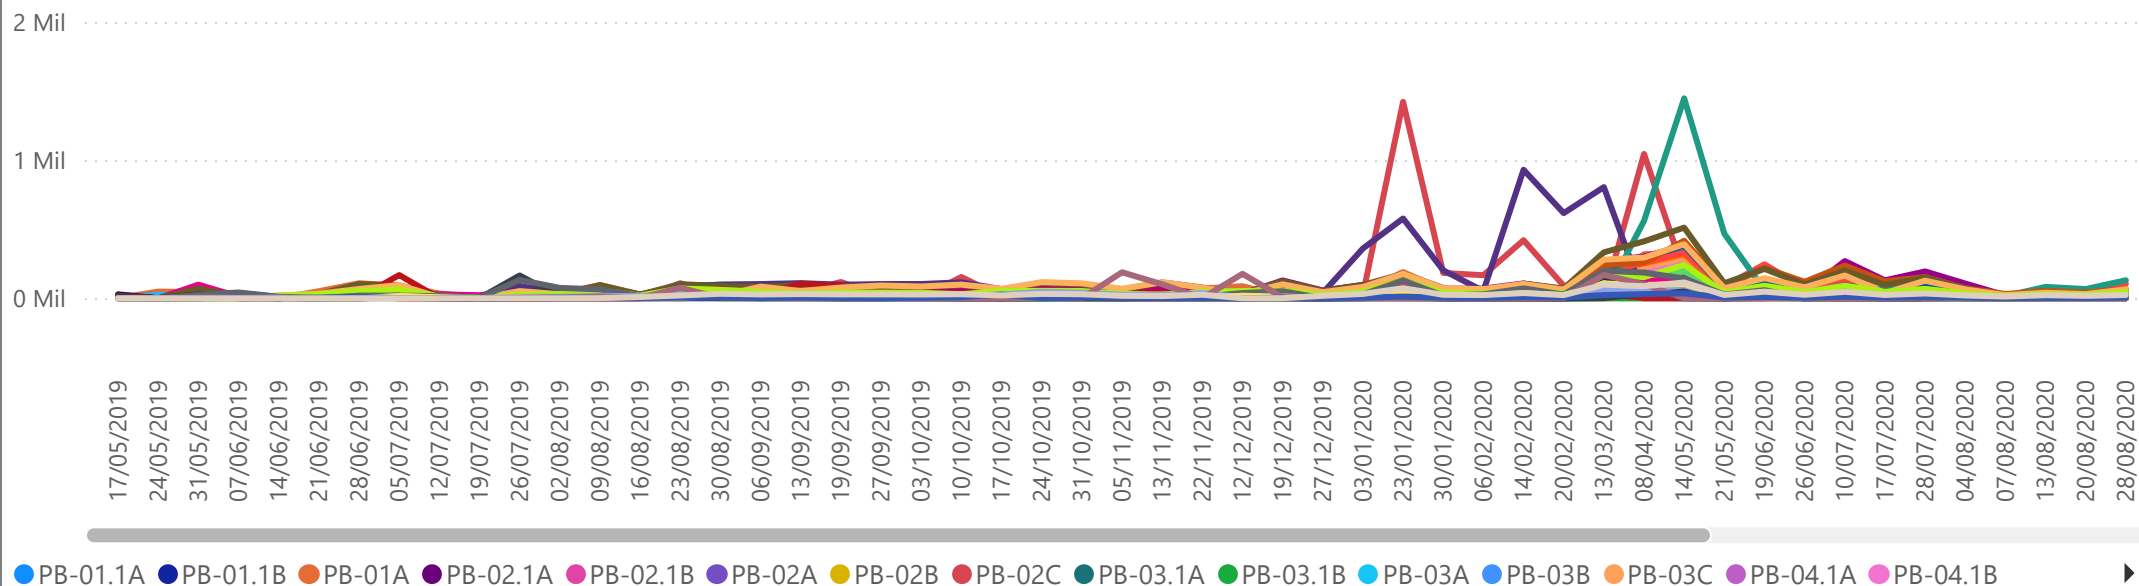

Regulador de Pressão (bar)

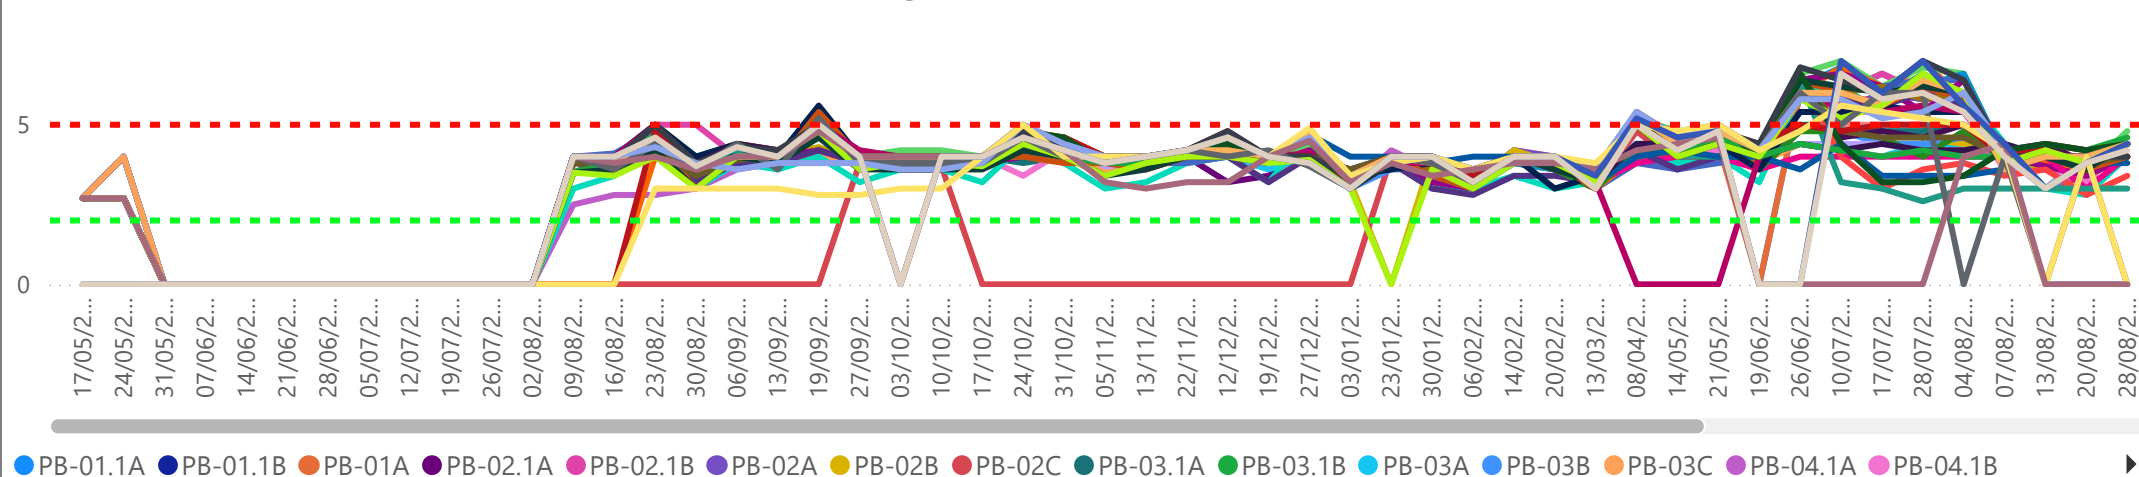

Média Rebaixamento por Aquífero, Distância da BH e PM

Média Rebaixamento

Média Rebaixamento por Aquífero, Distância da BH e PM

Média Rebaixamento

Média Rebaixamento por Aquífero, Distância da BH e PM

Média Rebaixamento

